


8.96 × 4.28 m • washers 1.05 × 1.02 • dryers 1.05 wide • nothing moves

Drawn to the dimensions supplied. Everything in colour is paint, signage or a bin — no machine, pipe or duct is relocated.

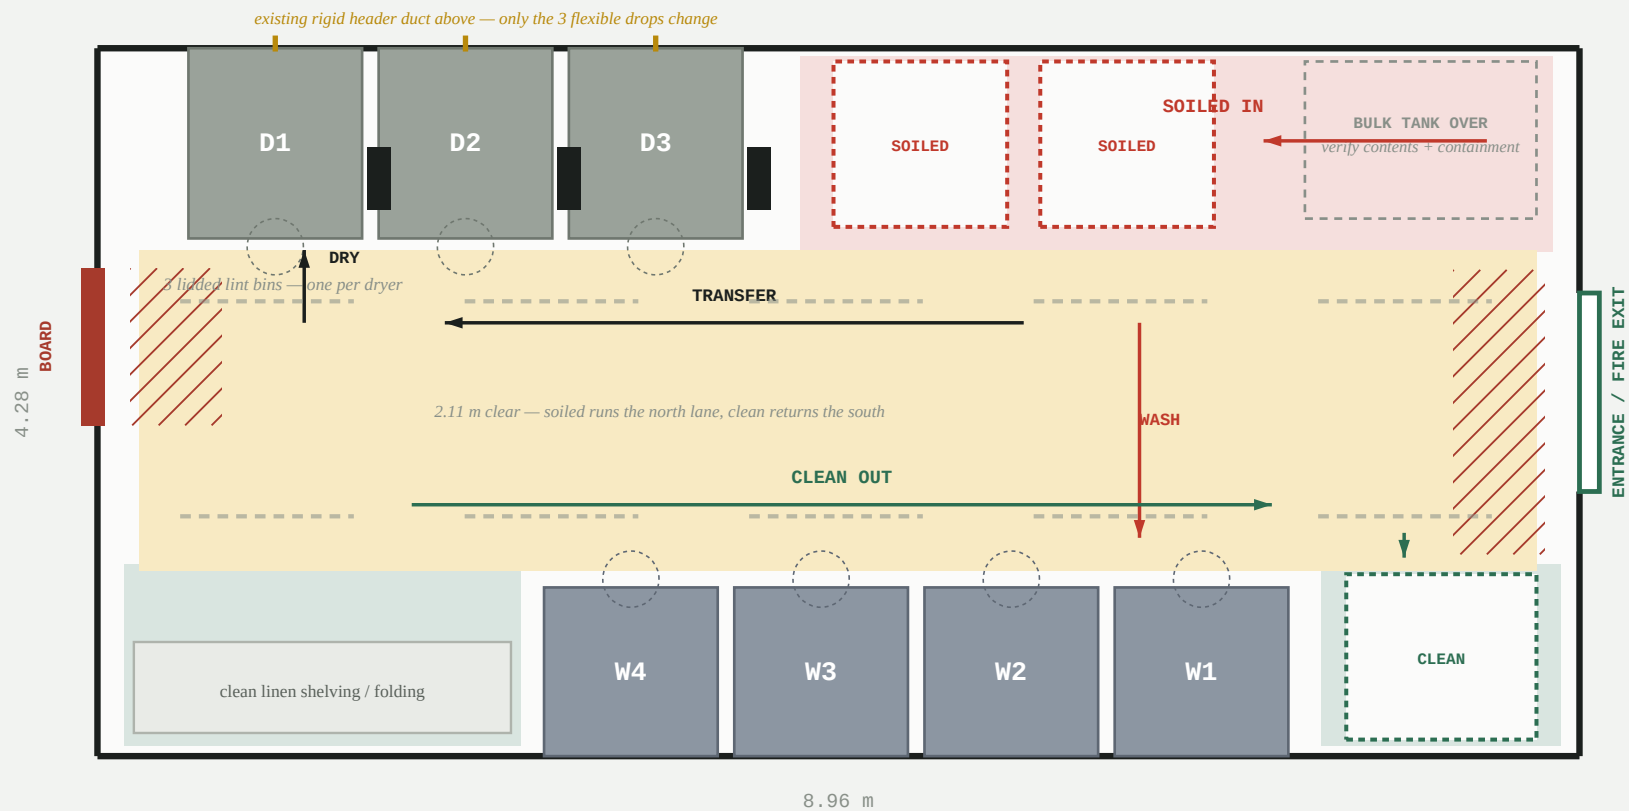

LEGEND — EVERYTHING BELOW IS PAINT, SIGNAGE OR A BIN

- | | | | |
|---|--|---|--|
| <div></div> Soiled side
receiving north-east, by the door | <div></div> Walkway
2.11 m clear, also the escape route | <div></div> Washer W1–W4
south wall, plumbed | One door
Soiled in and clean out share it,
separated by side, not by direction.
<i>So the doorway must never be blocked.</i> |
| <div></div> Clean side
staging south-east + folding south-west | <div></div> Keep clear
board and inside the door | <div></div> Dryer D1–D3
north wall, ducted | |
| | | <div></div> LED batten | |

Machine sizes are from your tape photos; positions along each wall are still read from the top view.
Machines occupy 2.17 m of the 4.28 m width, leaving 2.11 m clear — comfortably above the 1.20 m a circulation and escape route needs. Free wall: 4.76 m on the washer side, 5.81 m on the dryer side, which is where the soiled and clean zones go. One tape photo was sent twice, so one dryer dimension is still missing; if the dryer depth is 1.51 m rather than the 1.15 m drawn, the walkway becomes 1.75 m and still works.