


Dryers left, washers right · 2.11 m walkway · nothing moves

8.96 × 4.28 m. Washers 1.05 × 1.02, dryers 1.05 wide. Everything in colour is paint, signage or a bin — no machine, pipe or duct is relocated.

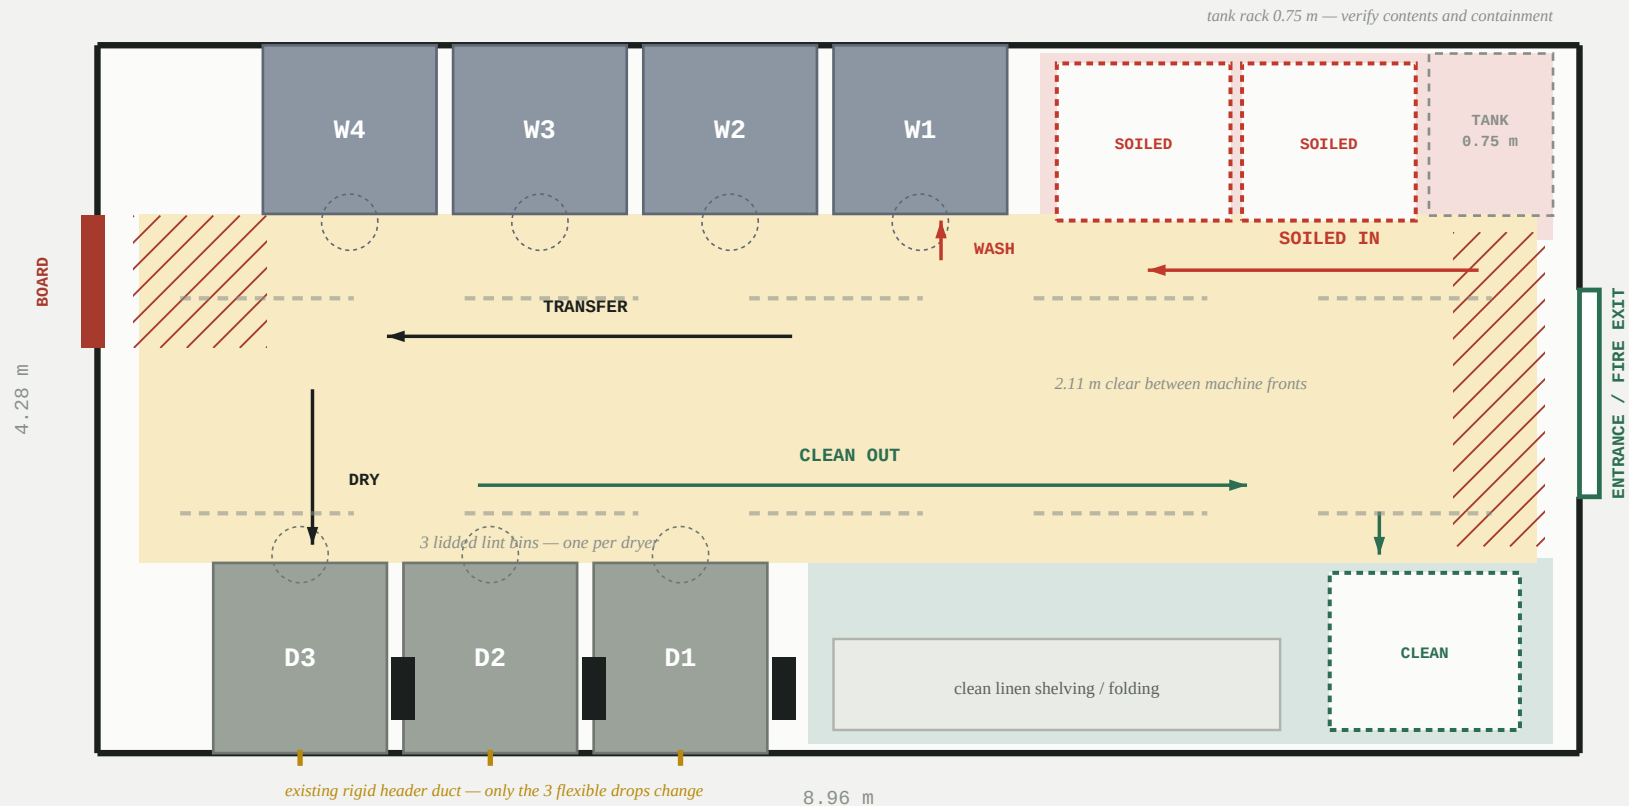

LEGEND — EVERYTHING BELOW IS PAINT, SIGNAGE OR A BIN

- | | | |
|--|--|---|
| <div></div> Soiled side
receiving north-east, feeds the washers | <div></div> Walkway
2.11 m clear, also the escape route | <div></div> Washer W1–W4
north wall — RIGHT as you enter |
| <div></div> Clean side
staging + folding south-east, off the dryers | <div></div> Keep clear
board and inside the door | <div></div> Dryer D1–D3
south wall — LEFT as you enter |
| | | <div></div> LED batten |

One door, and it works

Washers right, dryers left puts soiled and clean on opposite sides with no crossing except the wash-to-dry transfer at the far end.

The doorway must never be blocked.

Sides corrected: dryers on the left as you enter, washers on the right — which removes a crossing.

With the washers on the right and the dryers on the left, soiled feeds straight into the washers and clean comes straight off the dryers — the two never cross except once, at the far end, and that crossing is washed linen. Machines occupy 2.17 m of the 4.28 m width, leaving 2.11 m clear against the 1.20 m an escape route needs. Machine sizes are measured; positions along each wall are scaled from the top view, so mark the floor from the machines. One tape photo was duplicated, so one dryer dimension is still outstanding.